




 Curtain wall 3	630 SF
 CMU wall 5	938 SF
 Overhead hanging doors 2	2 EA
 Windows 4	4 EA

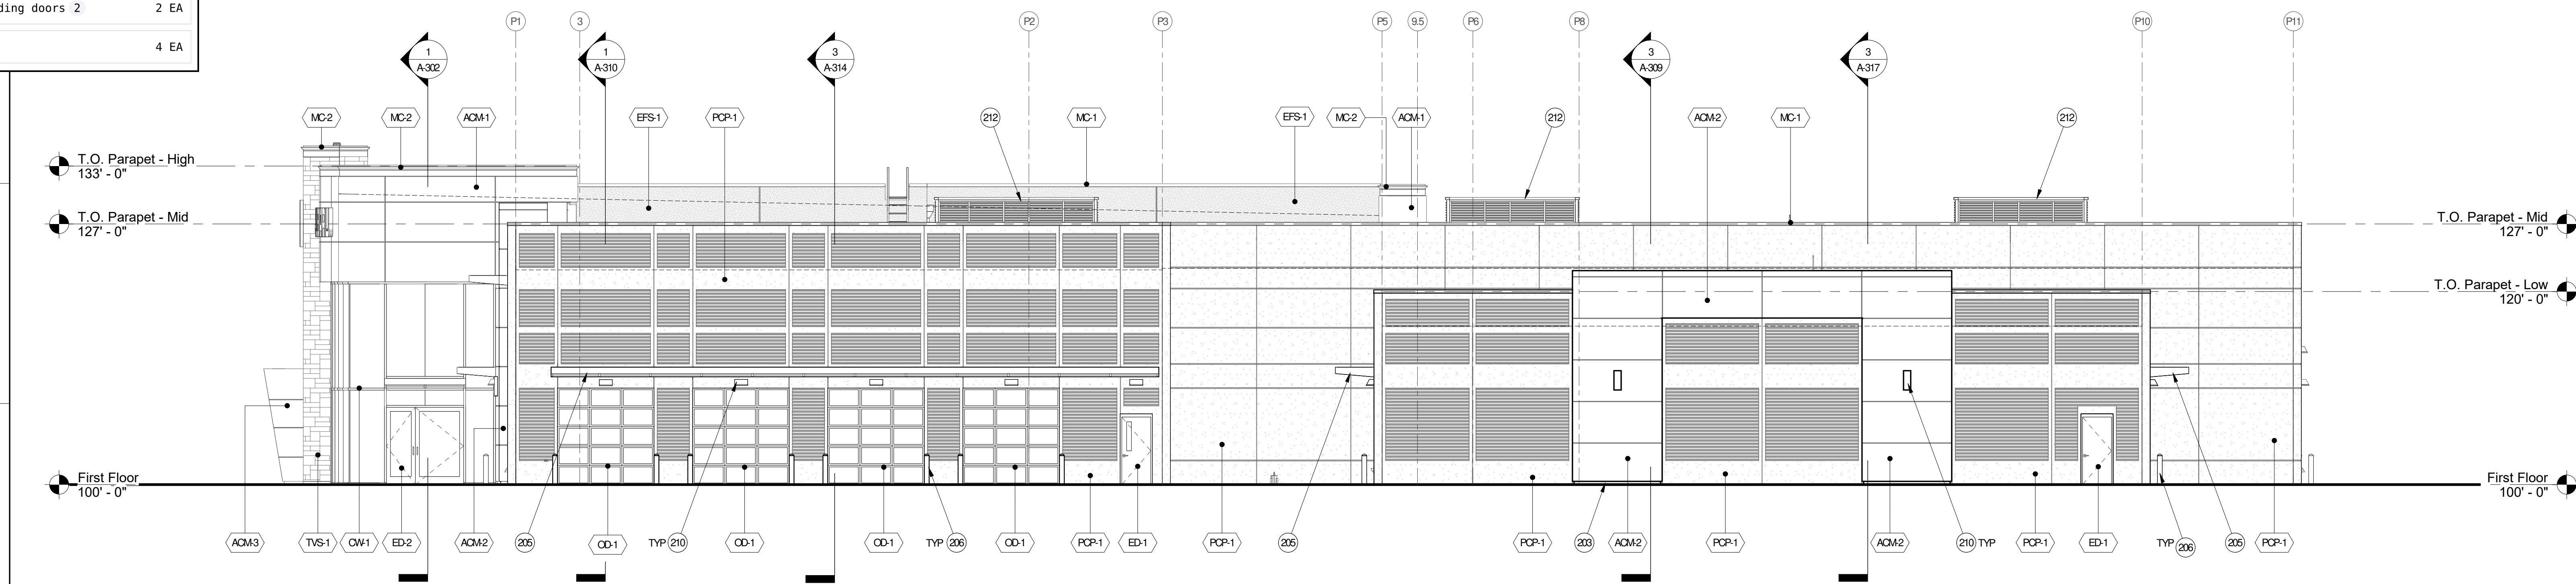

East Elevation **3**
1/8" = 1'-0"

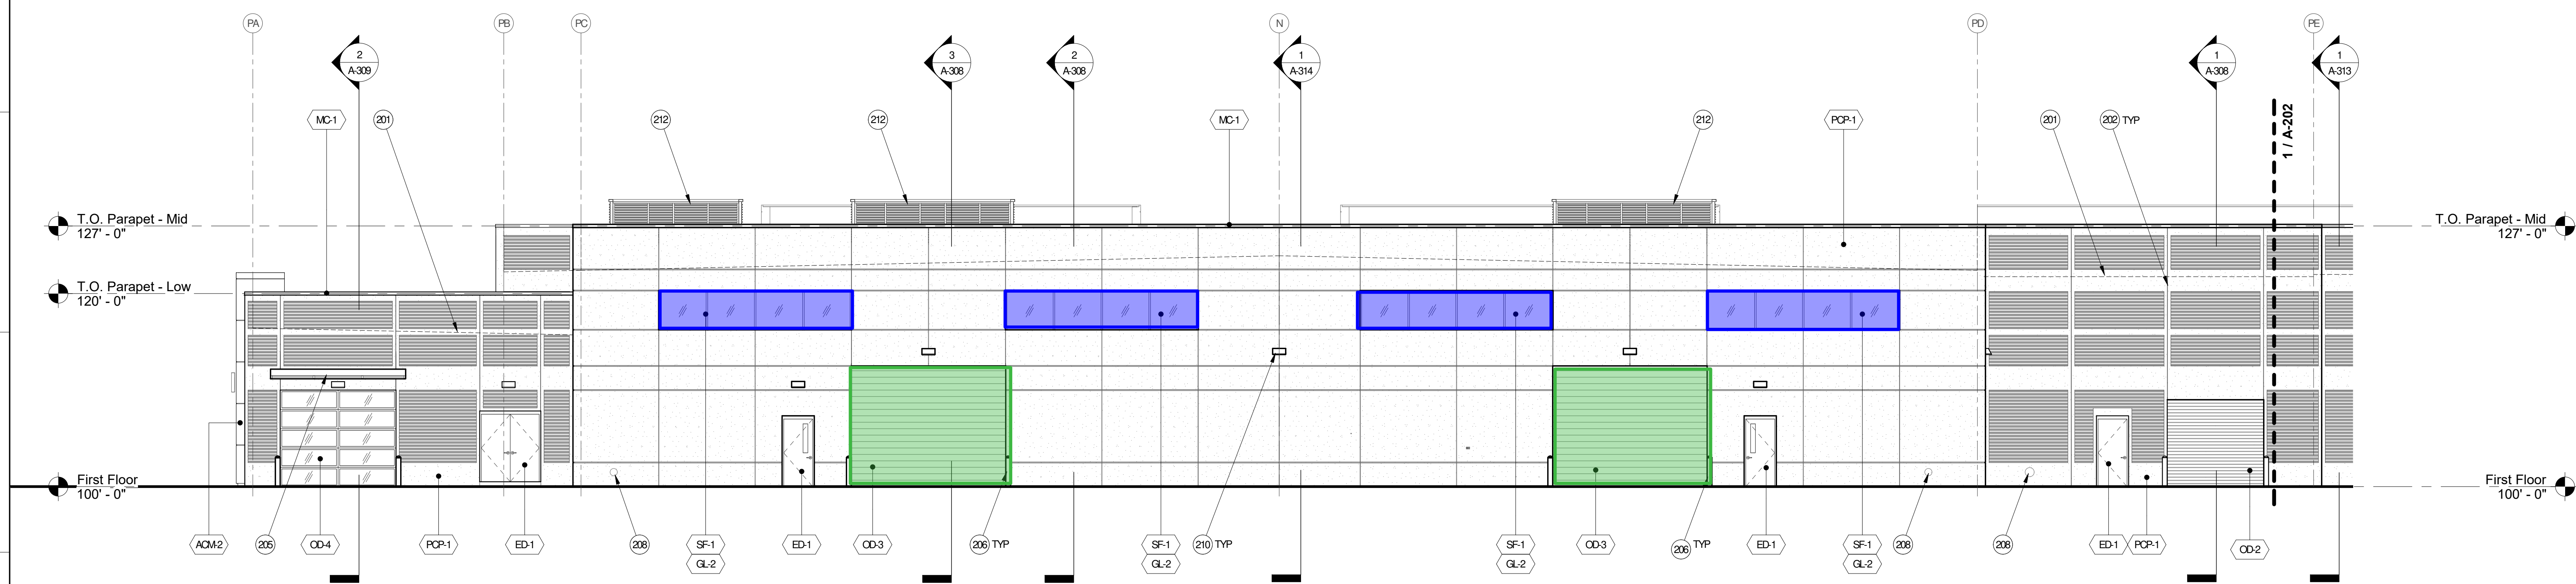

North Elevation - Area B 2

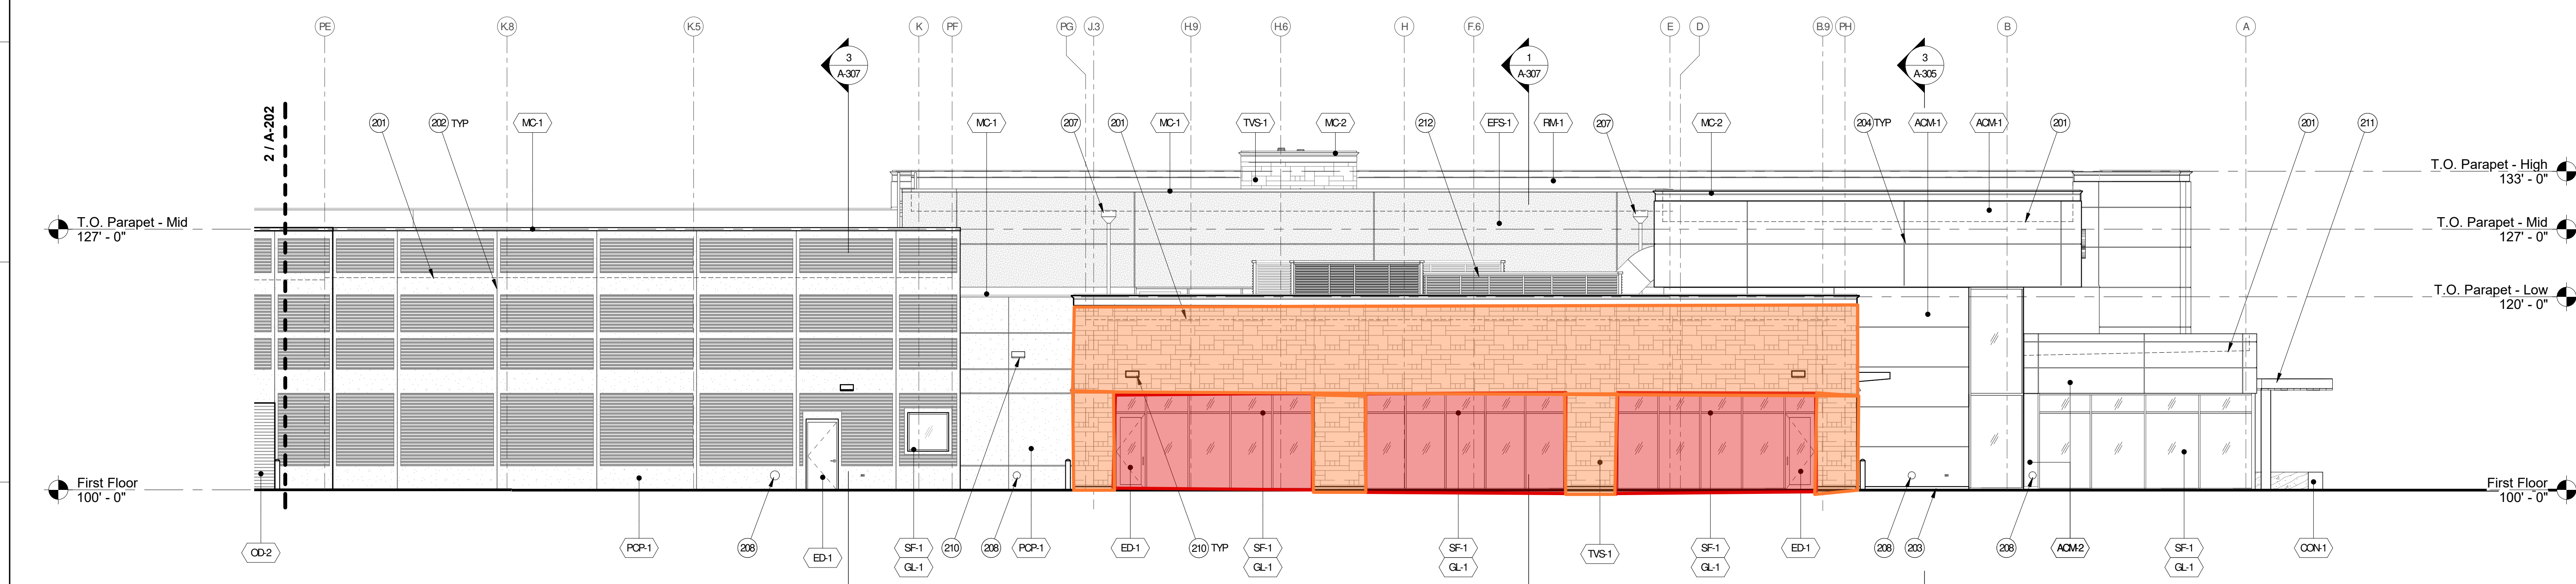

North Elevation - Area A 1
1/8" = 1'-0"

MATERIALS	
AO-M1	ALUMINUM COMPOSITE PANEL WALL SYSTEM MANUFACTURER: ALCOLIC CO. B&K SYSTEM
AO-M2	ALUMINUM COMPOSITE PANEL WALL SYSTEM MANUFACTURER: ALCOLIC CO. MCM-MS GREY
AO-M3	ALUMINUM COMPOSITE PANEL WALL SYSTEM MANUFACTURER: ALCOLIC CO. PIMENTO COZZI GREY
OW-1	ARCHITECTURAL CAST IN PLACE CONCRETE SEAT WALL WITH FORMLINER
OW-1	ALUMINUM CURTAIN WALL SYSTEM2 MANUFACTURER: KAWNEER 1800 SYSTEM2 COLOR/FINISH: CLEAR ANODIZED (SEE FRAME ELEVATIONS)
ED-1	EXTERIOR ALUMINUM SLIDING GLASS DOOR WITH HIGH PERFORMANCE COATING COLOR: T80 (SEE DOOR SCHEDULE)
ED-2	EXTERIOR ALUMINUM SLIDING DOOR (DOORS) MANUFACTURER: KAWNEER MID-STYLE COLOR: CLEAR ANODIZED (SEE DOOR SCHEDULE)
EPS-1	EXTERIOR INSULATION FINISH SYSTEM MANUFACTURER: STUCCO CORPORATION FINE LINE TEXTURE COLOR: MATCH AO-M1
GL-1	GLASS INSULATED DOUBLE GLAZING
GL-2	TRANSlucent GLASS INSULATED DOUBLE GLAZING
MC-1	PRE-FINISH METAL CLADDING AND SHEET METAL FLASHING MANUFACTURER: BERTRIDGE MFG. CO. LEAD COAT
MC-2	PRE-FINISH ALUMINUM COMPOUND ASSEMBLY WITH TOP COAT AND CUSTOM FLASHPASTE. FACE TO BE PAINTED. REMINDER OF METAL TO BE SILVER METALLIC FINISH
MC-3	PRE-FINISH ALUMINUM
D-1	ALUMINUM FRAME GLASS OVERHEAD DOOR COLOR/FINISH: CLEAR ANODIZED (SEE DOOR SCHEDULE - OCPA)
D-2	INSULATED COILING STEEL OVERHEAD DOOR FINISH: FACTORY FINISH COLOR: MATCH EXTERIOR MAIN DOORS (SEE DOOR SCHEDULE - OPCS)
D-3	ALUMINUM AND CLEAR ACRYLIC POLYCARBONATE HIGH SPEED ROLL UP DOOR COLOR: DOOR SCHEDULE (OVC)
D-4	ALUMINUM FRAME OVERHEAD DOOR WITH POLYCARBONATE GLAZING COLOR: FINISH: CLEAR ANODIZED (SEE DOOR SCHEDULE (OCPA))
PCP-1	PRECAST INTEGRAL COLOR CONCRETE WALL PANEL WITH ADJUSTABLE FINISH (LIGHT AGGREGATE EXPOSURE) FILTERED LIGHT/1:400/FILTERED RB 1:6 A-107 & A-108
RM-1	ROOF MEMBRANE AT BACK SIDE OF PARAPET COLOR: GRAY
SF-1	ALUMINUM SLIDING SYSTEM MANUFACTURER: KAWNEER TR-FAB VERSAPAGE 4511 COLOR: CLEAR ANODIZED (SEE FRAME ELEVATIONS)
VS-1	THIN VEINER SLATE MANUFACTURER: OMAHA SLATE PRODUCTS COLOR: SHADOW GREY

KEYNOTES

201	LINE OF ROOF BEYOND PARAPET
202	PRECAST PANEL JOINT WITH SEALANT
203	CAST IN PLACE CONCRETE WALL CURB WITH TEXTURED ACRYLIC COATING COLOR: TB-110
204	ACM/PANEL JOINT REVEAL
205	PREFABRICATED OPEN/CLOSERED ALUMINUM CANOPY PANEL SECTIONS
206	6" HD GALVANIZED CONCRETE FILLED STEEL PIPE BOLLARD WITH H+P COATING COLOR: TB-10
207	THRU-WALL SQUIPPER WITH PRE-FINISHED METAL CONDUIT HEAD AND DOWNSPOUT, COLOR: LEAD COLE (SEE WALL SECTIONS)
208	ROOF DRAIN OVERFLOW DISCHARGE, RE-FLUAGING
209	INTERNALLY ILLUMINATED BUILDING UNIT SERVICE BY OWNER
210	WALL MOUNTED EXTERIOR LIGHTING RE-ELECTRICAL
211	PRE-FINISHED ALUMINUM PLANK CANOPY SYSTEM MANUFACTURER: AVIDOR COLOR: CLEAR ANODIZED FRAMING, WOOD GRAIN POWDER COAT FINISH
212	PRE-FINISHED PLASTIC/CLOSERED SLOPED WALL DIRECT MOUNTED TO ROOF TOP UNITS COLOR: TB-10