


Total areas		
	Fingerprint 1	6,753 SF
	Net area 22	6,043 SF
	Doors area 19	44 SF
	Gross area 20	6,721 SF
	Gross Internal Area ...	206,237 SF
Total lines		
	Doors centerline 19	61 FT
	Wall centerline 142	1,030 FT
	Wall Perimeter 22	1,406 FT
Total counts		
	Toilet 2	2 EA
	Sink 4	4 EA
	Single Swing Door 21	21 EA
	Window/Curtain Wall/Facade 3	49 SF

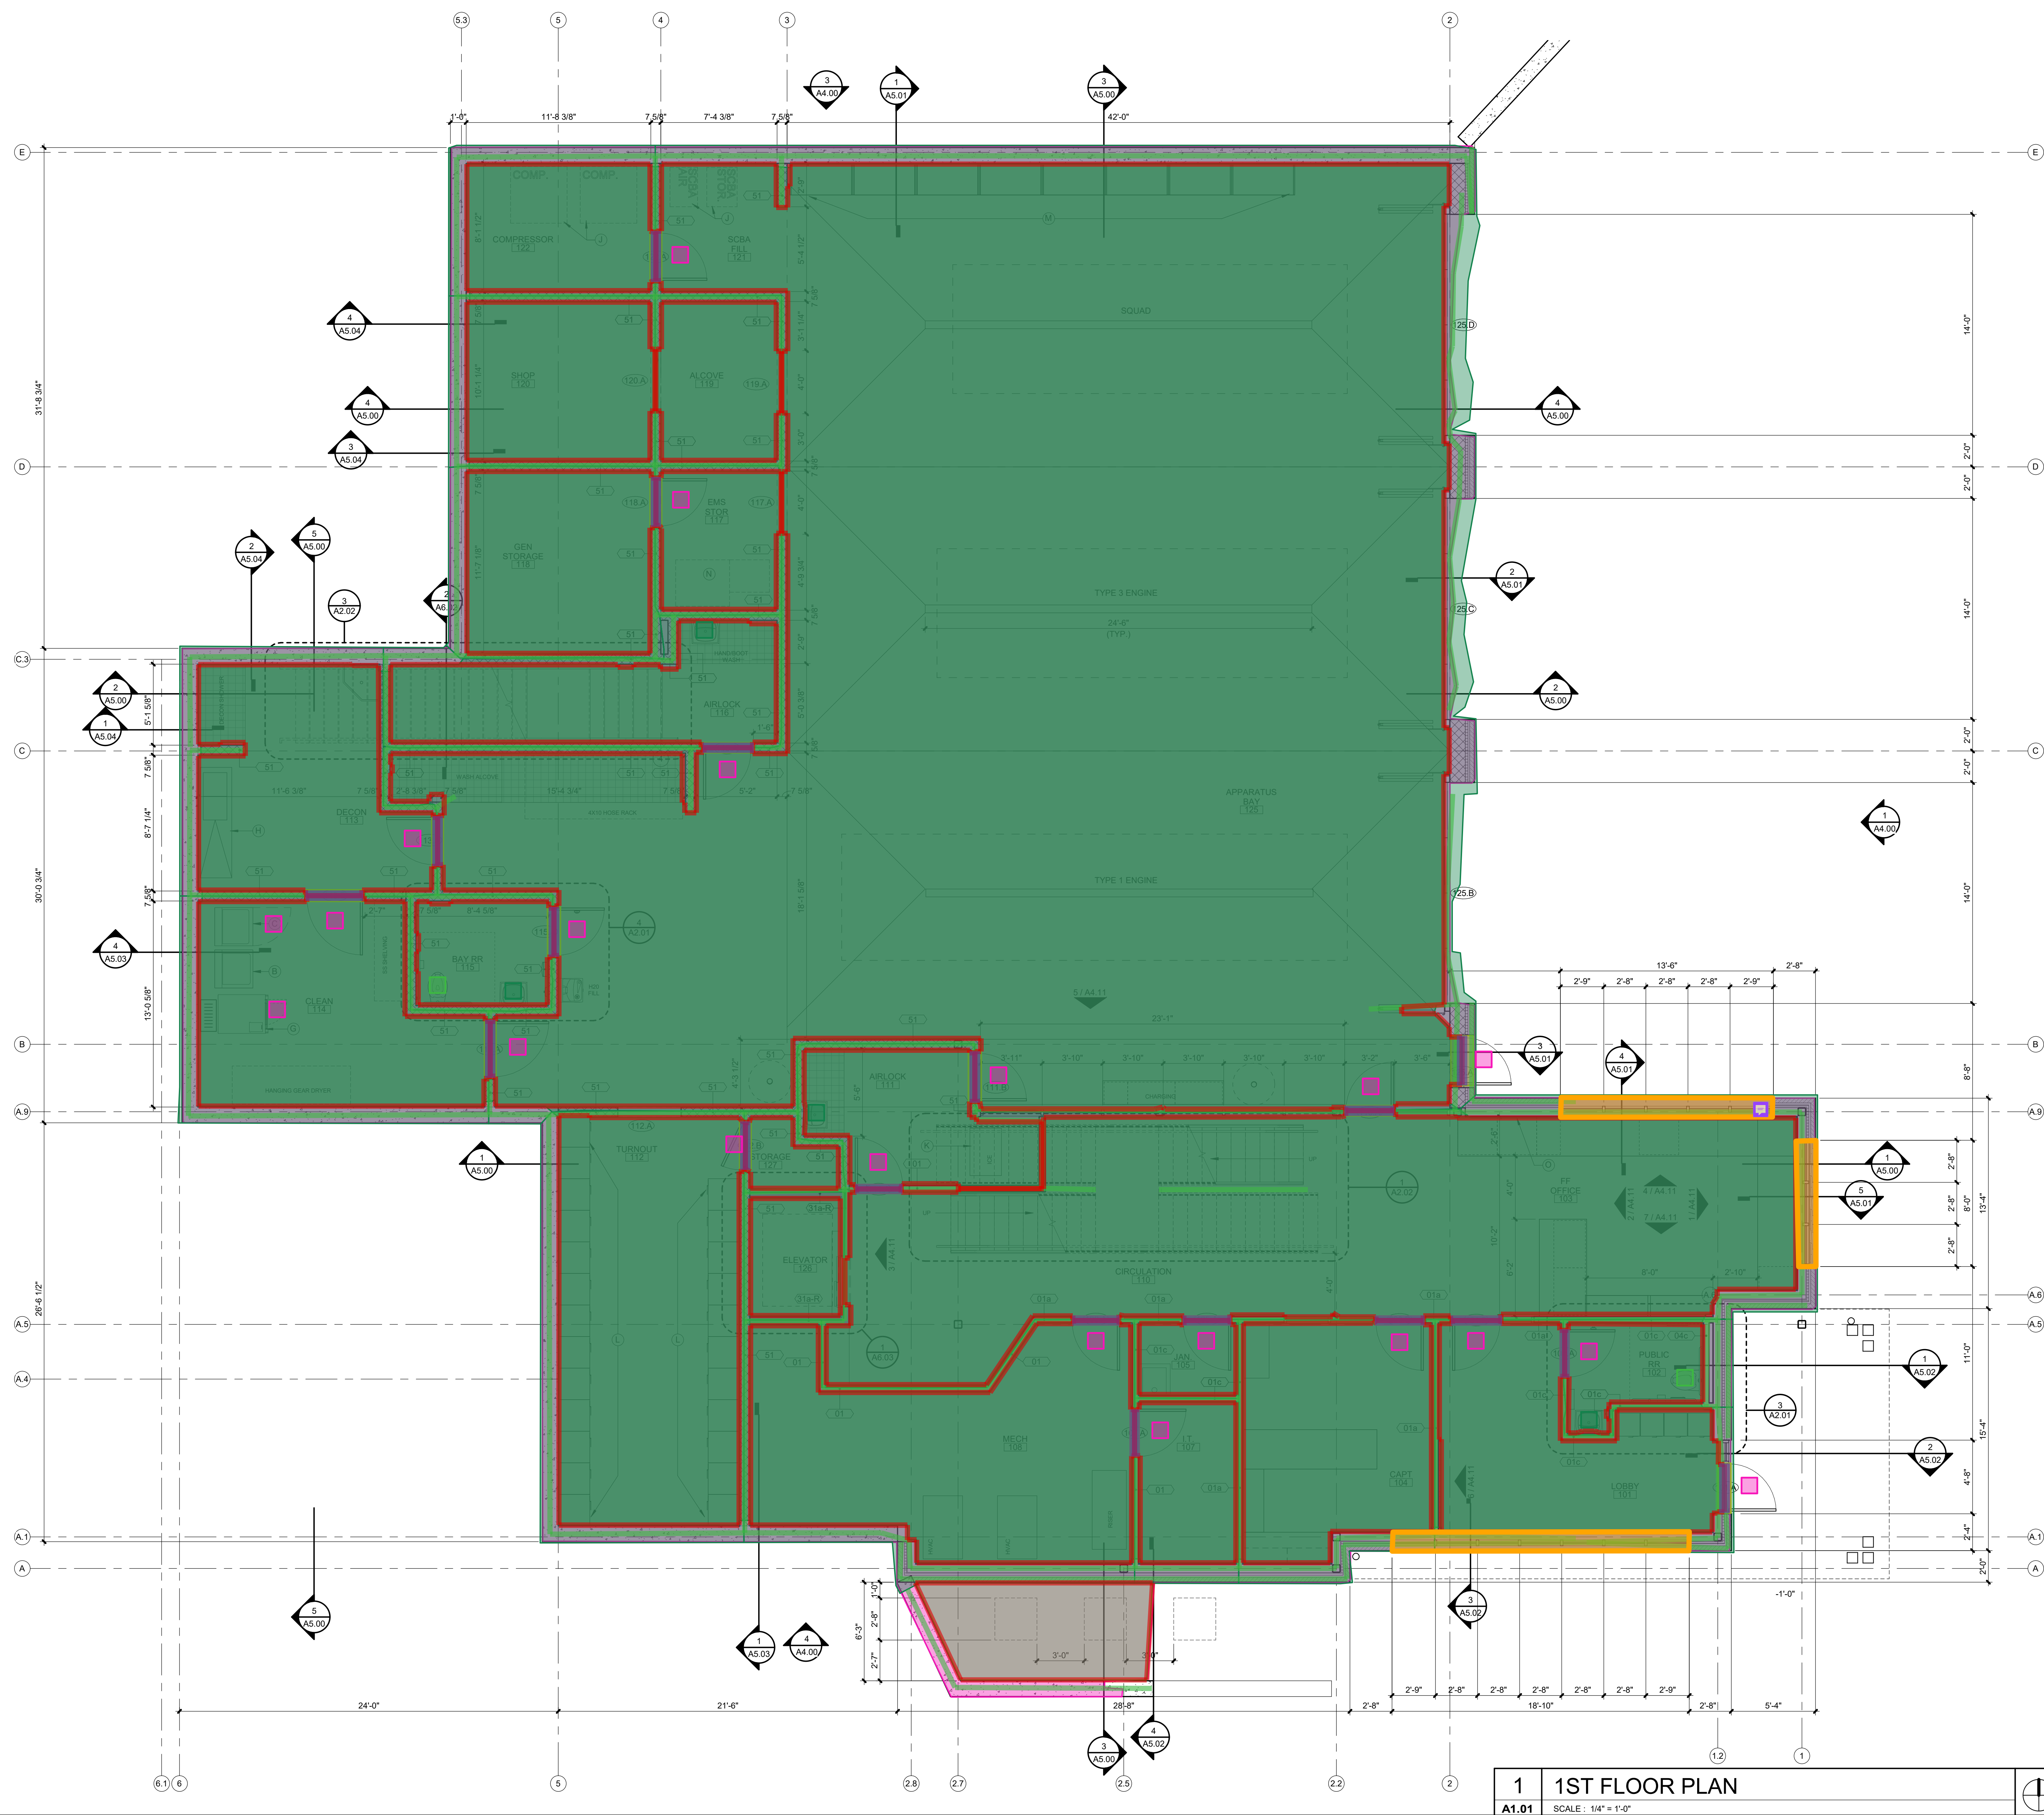

**Olathe Fire
Station No. 8**
14700 Lakeshore Dr
Olathe KS



Project No.:	19003
Date:	02.17.2020
Issued For:	DESIGN DEVELOPMENT

[illegible]

REGISTRATION

NOT FOR CONSTRUCTION

PROJECT TEAM	
ARCHITECT	FINKLE-WILLIAMS ARCHITECTURE
FIRE STATION CONSULTANT	TCA ARCHITECTURE
CIVIL	SK DESIGN GROUP
LANDSCAPE	SWT DESIGN
STRUCTURAL	BOB D. CAMPBELL
PLUMBING	LANKFORD FENDLER
MECHANICAL	LANKFORD FENDLER
ELECTRICAL	LANKFORD FENDLER
CONTRACTOR	TURNER CONSTRUCTION

FINKLE + WILLIAMS
ARCHITECTURE

7007 College Blvd, Suite 411
Overland Park, Kansas 66211
913+498-1550

SHEET TITLE

FIRST FLOOR
PLAN

SHEET NUMBER

A1.01

C:\Users\fofster\Documents\Claira_F58-NEW_Control_F18_elliffoester.nt

