


Total areas		
Footprint 1	733 SF	
Net area 13	617 SF	
Doors area 1	1 SF	
Gross area 12	664 SF	
Gross Internal Area (GIA)	12591 SF	
Total counts		
Doors centerline 1	2 FT	
Wall centerline 58	240 FT	
Wall Perimeter 14	385 FT	
Total counts		
Single Swing Door 14	14 EA	
Windows 8	8 EA	

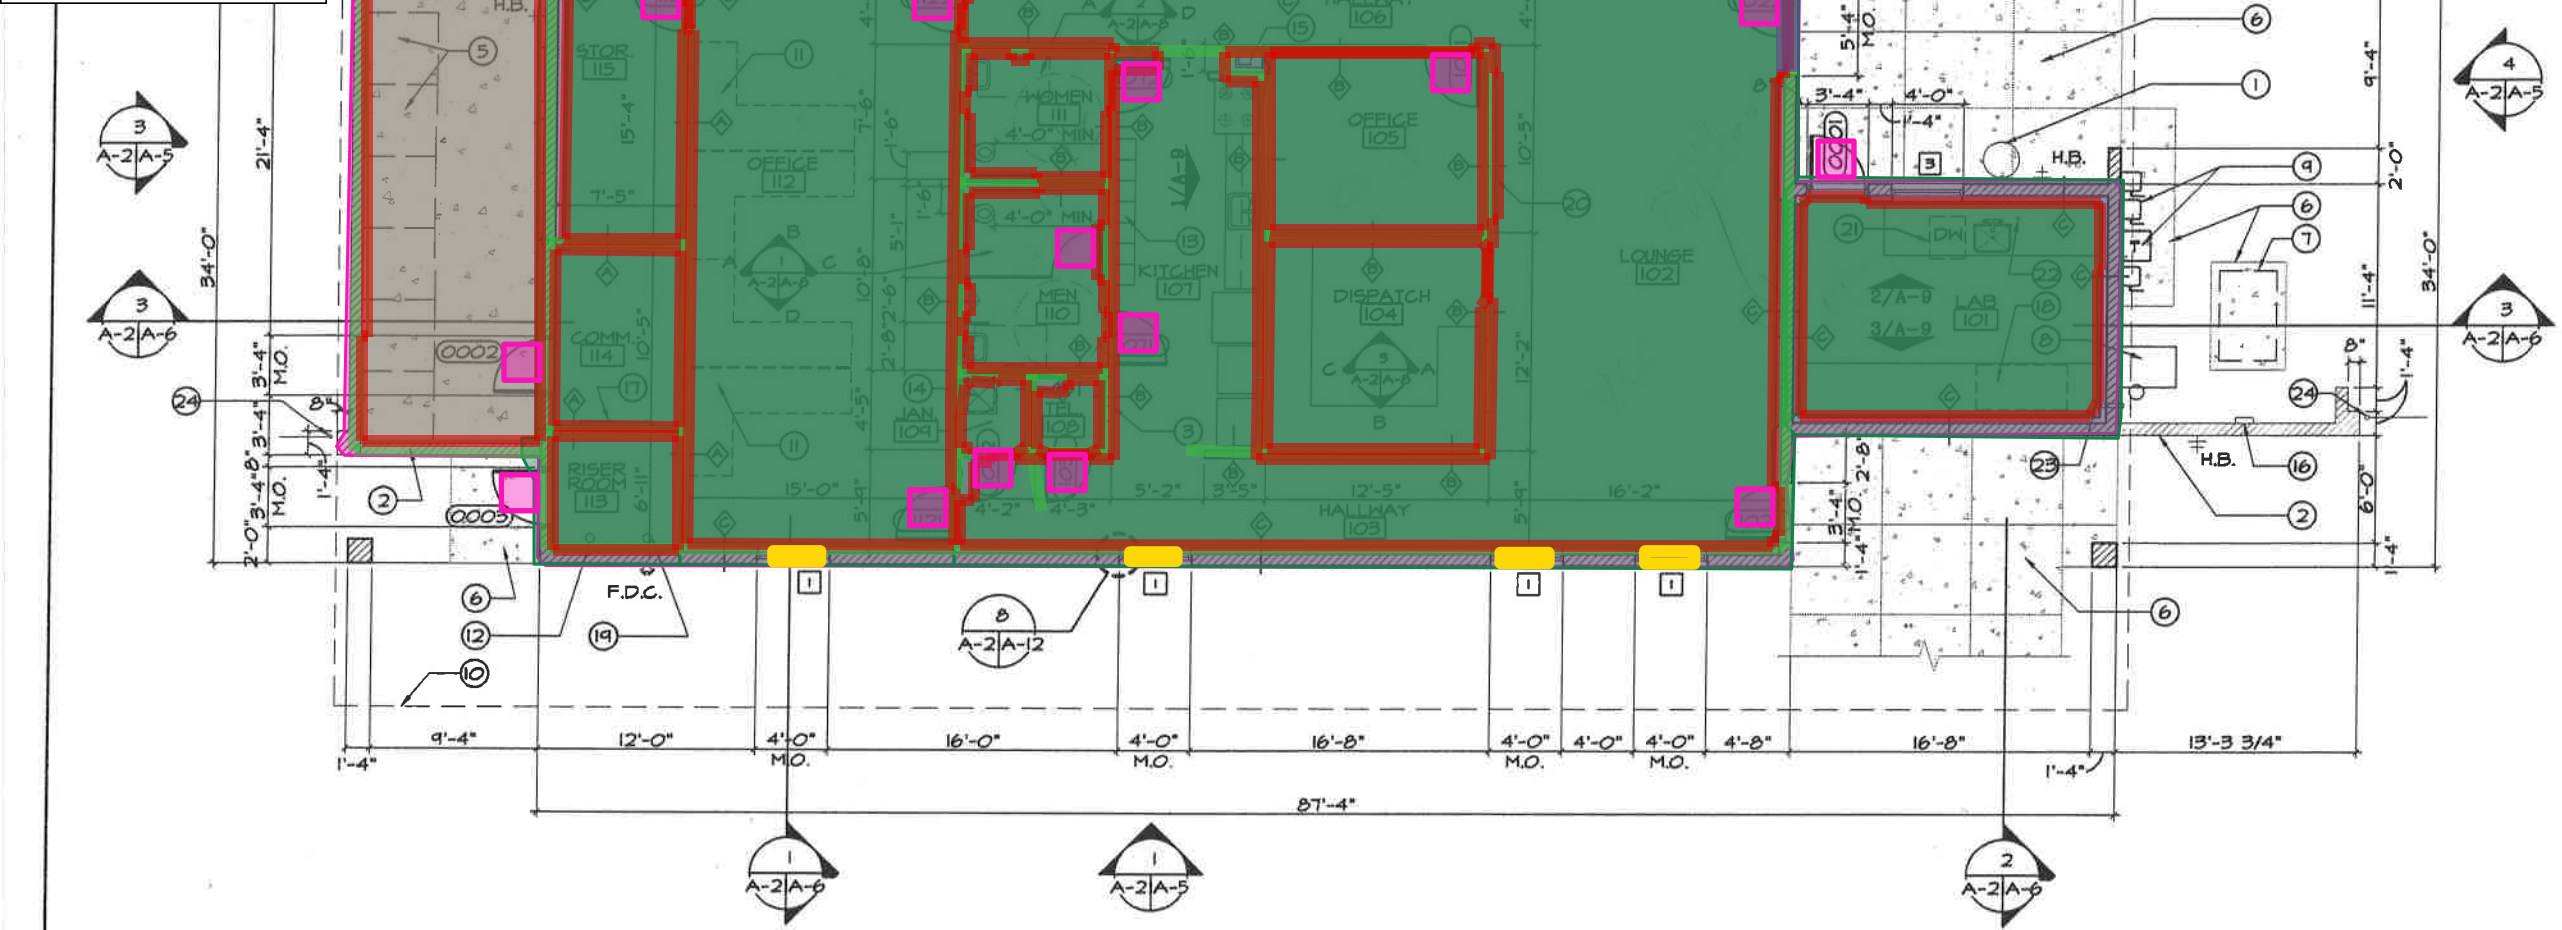

- FLOOR PLAN KEY NOTES**
- 1 OUTDOOR SHOWER AND EYEWASH
 - 2 CMU SCREEN WALL- SEE ELEVATIONS FOR HEIGHT
 - 3 ELECTRICAL PANELS FLUSH MOUNTED IN 6" STUD WALL
 - 4 GROUND MOUNTED HEAT PUMP UNITS- REFER TO MECHANICAL DRAWINGS
 - 5 OUTDOOR PALLET RACK STORAGE
 - 6 CONCRETE PAD / WALK
 - 7 GROUND MOUNTED CONDENSING UNIT- REFER TO MECHANICAL DRAWINGS
 - 8 WALL MOUNTED EXHAUST FAN- REFER TO MECHANICAL DRAWINGS
 - 9 ELECTRICAL SERVICE- REFER TO ELECTRICAL DRAWINGS
 - 10 LINE OF ROOF OVERHANG
 - 11 SYSTEMS FURNITURE (N.I.C.)
 - 12 DOMESTIC WATER RISER- REFER TO PLUMBING DRAWINGS
 - 13 LOCKERS- REFER TO SPECIFICATIONS
 - 14 FLOOR MOP SINK WITH 20 GAL. WATER HEATER MOUNTED ABOVE- REFER TO PLUMBING DRAWINGS
 - 15 ELECTRIC DRINKING FOUNTAIN
 - 16 IRRIGATION CONTROLLER
 - 17 TELEPHONE MOUNTING BOARD
 - 18 5' LONG EXHAUST HOOD
 - 19 FIRE SPRINKLER RISER
 - 20 BULLETIN BOARD (SUPPLIED BY OWNER, INSTALLED BY CONTRACTOR)
 - 21 DISHWASHER (SUPPLIED BY OWNER, INSTALLED BY CONTRACTOR)
 - 22 COUNTER MOUNTED EYEWASH
 - 23 1" SLEEVE THRU WALL FOR FUEL DRAIN @ 30" A.F.F.
 - 24 SECURITY FENCE- 2"Ø SCHEDULE 40 PIPE IN CONCRETE FOOTING, REFER TO DETAIL 9/A-10. CENTER PIPE 1'-0" BACK FROM FACE OF MASONRY WALL

1 FLOOR PLAN
SCALE: 3/16" = 1'-0"

WALL LEGEND		
TYPE	DETAIL	DESCRIPTION
		EXTERIOR 8" CMU WALL
	2/A-II	INTERIOR PARTITION- 5/8" TYPE 'X' GYP. BD. BOTH SIDES 3-5/8" METAL STUD FRAMING, EXTEND TO ROOF STRUCTURE. PROVIDE R-II BATT INSULATION.
	3/A-II	INTERIOR PARTITION- 5/8" TYPE 'X' GYP. BD. BOTH SIDES 3-5/8" METAL STUD FRAMING, EXTEND WALL TO 9'-6" A.F.F.. PROVIDE R-II BATT INSULATION.
	4/A-II	INTERIOR PARTITION- FURR OUT CMU WALL W 5/8" TYPE 'X' GYP. BD. OVER 3-5/8" METAL STUD FRAMING. PROVIDE SPRAY-ON INSULATION. FRAMING AND INSULATION TO EXTEND TO BOTTOM OF ROOF TRUSSES. PROVIDE TYPE W.R. GYP. BD. AT RESTROOM SIDE OF INTERIOR PARTITIONS

DEPARTMENT OF THE NAVY SAN DIEGO		NAVAL FACILITIES ENGINEERING COMMAND SOUTHWEST DIVISION NAVAL FACILITIES CALIFORNIA		SUBMITTED: DESIGN: DRAWN: CHECKED: FP:		SATISFACTORY TO:		REVISIONS				
						DATE	DATE	APPROVED	DATE	PREP. BY	DESCRIPTION	SYMBOL
SIZE D IF SHEET IS LESS THAN 22" X 34" IT IS A REDUCED PRINT— SCALE REDUCED ACCORDINGLY				YU-0013R2 FUEL FARM BUILDING MARINE CORPS AIR STATION YUMA		FAC MANC. OFFICER:		DATE				
								DIRECTOR OF ENG.:				
								FP:				
								SW DIV FOR COMMANDER NAVFAC		DATE		
								FLOOR PLAN				
PWO. NO.				PROJECT LOCATION								
CONSTR. CONTRACT NO.												
SPEC.												
NAVFAC DRAWING NO.												
SHEET 14 OF												
A-2												

A hand-drawn floor plan of a rectangular room. The walls are represented by solid black lines. A green horizontal line runs across the bottom portion of the room, likely representing a baseboard or a specific material boundary. Several circular symbols are placed around the room:

- Top Left:** A circle containing the number "1" above the code "A-3/A-6".
- Bottom Left:** A circle containing the number "1" above the code "A-3/A-13". Below it, the text "RETURN AIR VENT- REFER TO MECHANICAL" is written.
- Center:** Two circles, each containing the number "1" above the code "A-3/A-6". They are connected by a vertical line. To their right, two lines point to the ceiling area with labels "GYF. BD. CEILING" and "EXHAUST FAN".
- Right Side:** A circle containing the number "2" above the code "A-3/A-6". To its left, a line points to the ceiling area with the label "2'x4' SUSPENDED GRID CEILING W/ SECOND LOOK ACUOSTICAL LAY-IN TILES".

The drawing is a technical sketch, likely for construction or renovation purposes, showing the placement of mechanical components and structural elements relative to a room's geometry.



--	--