


 Footprint 1	18,648 SF
 Net area 4	17,676 SF
 Gross area 8	20,387 SF
 Gross Internal Area... 2	8,250 SF
Total lines	
 Wall centerline 143	1,157 FT
 Wall Perimeter 10	1,534 FT
F1 6	6 EA
F2 14	14 EA
F3 10	10 EA
F4 3	3 EA

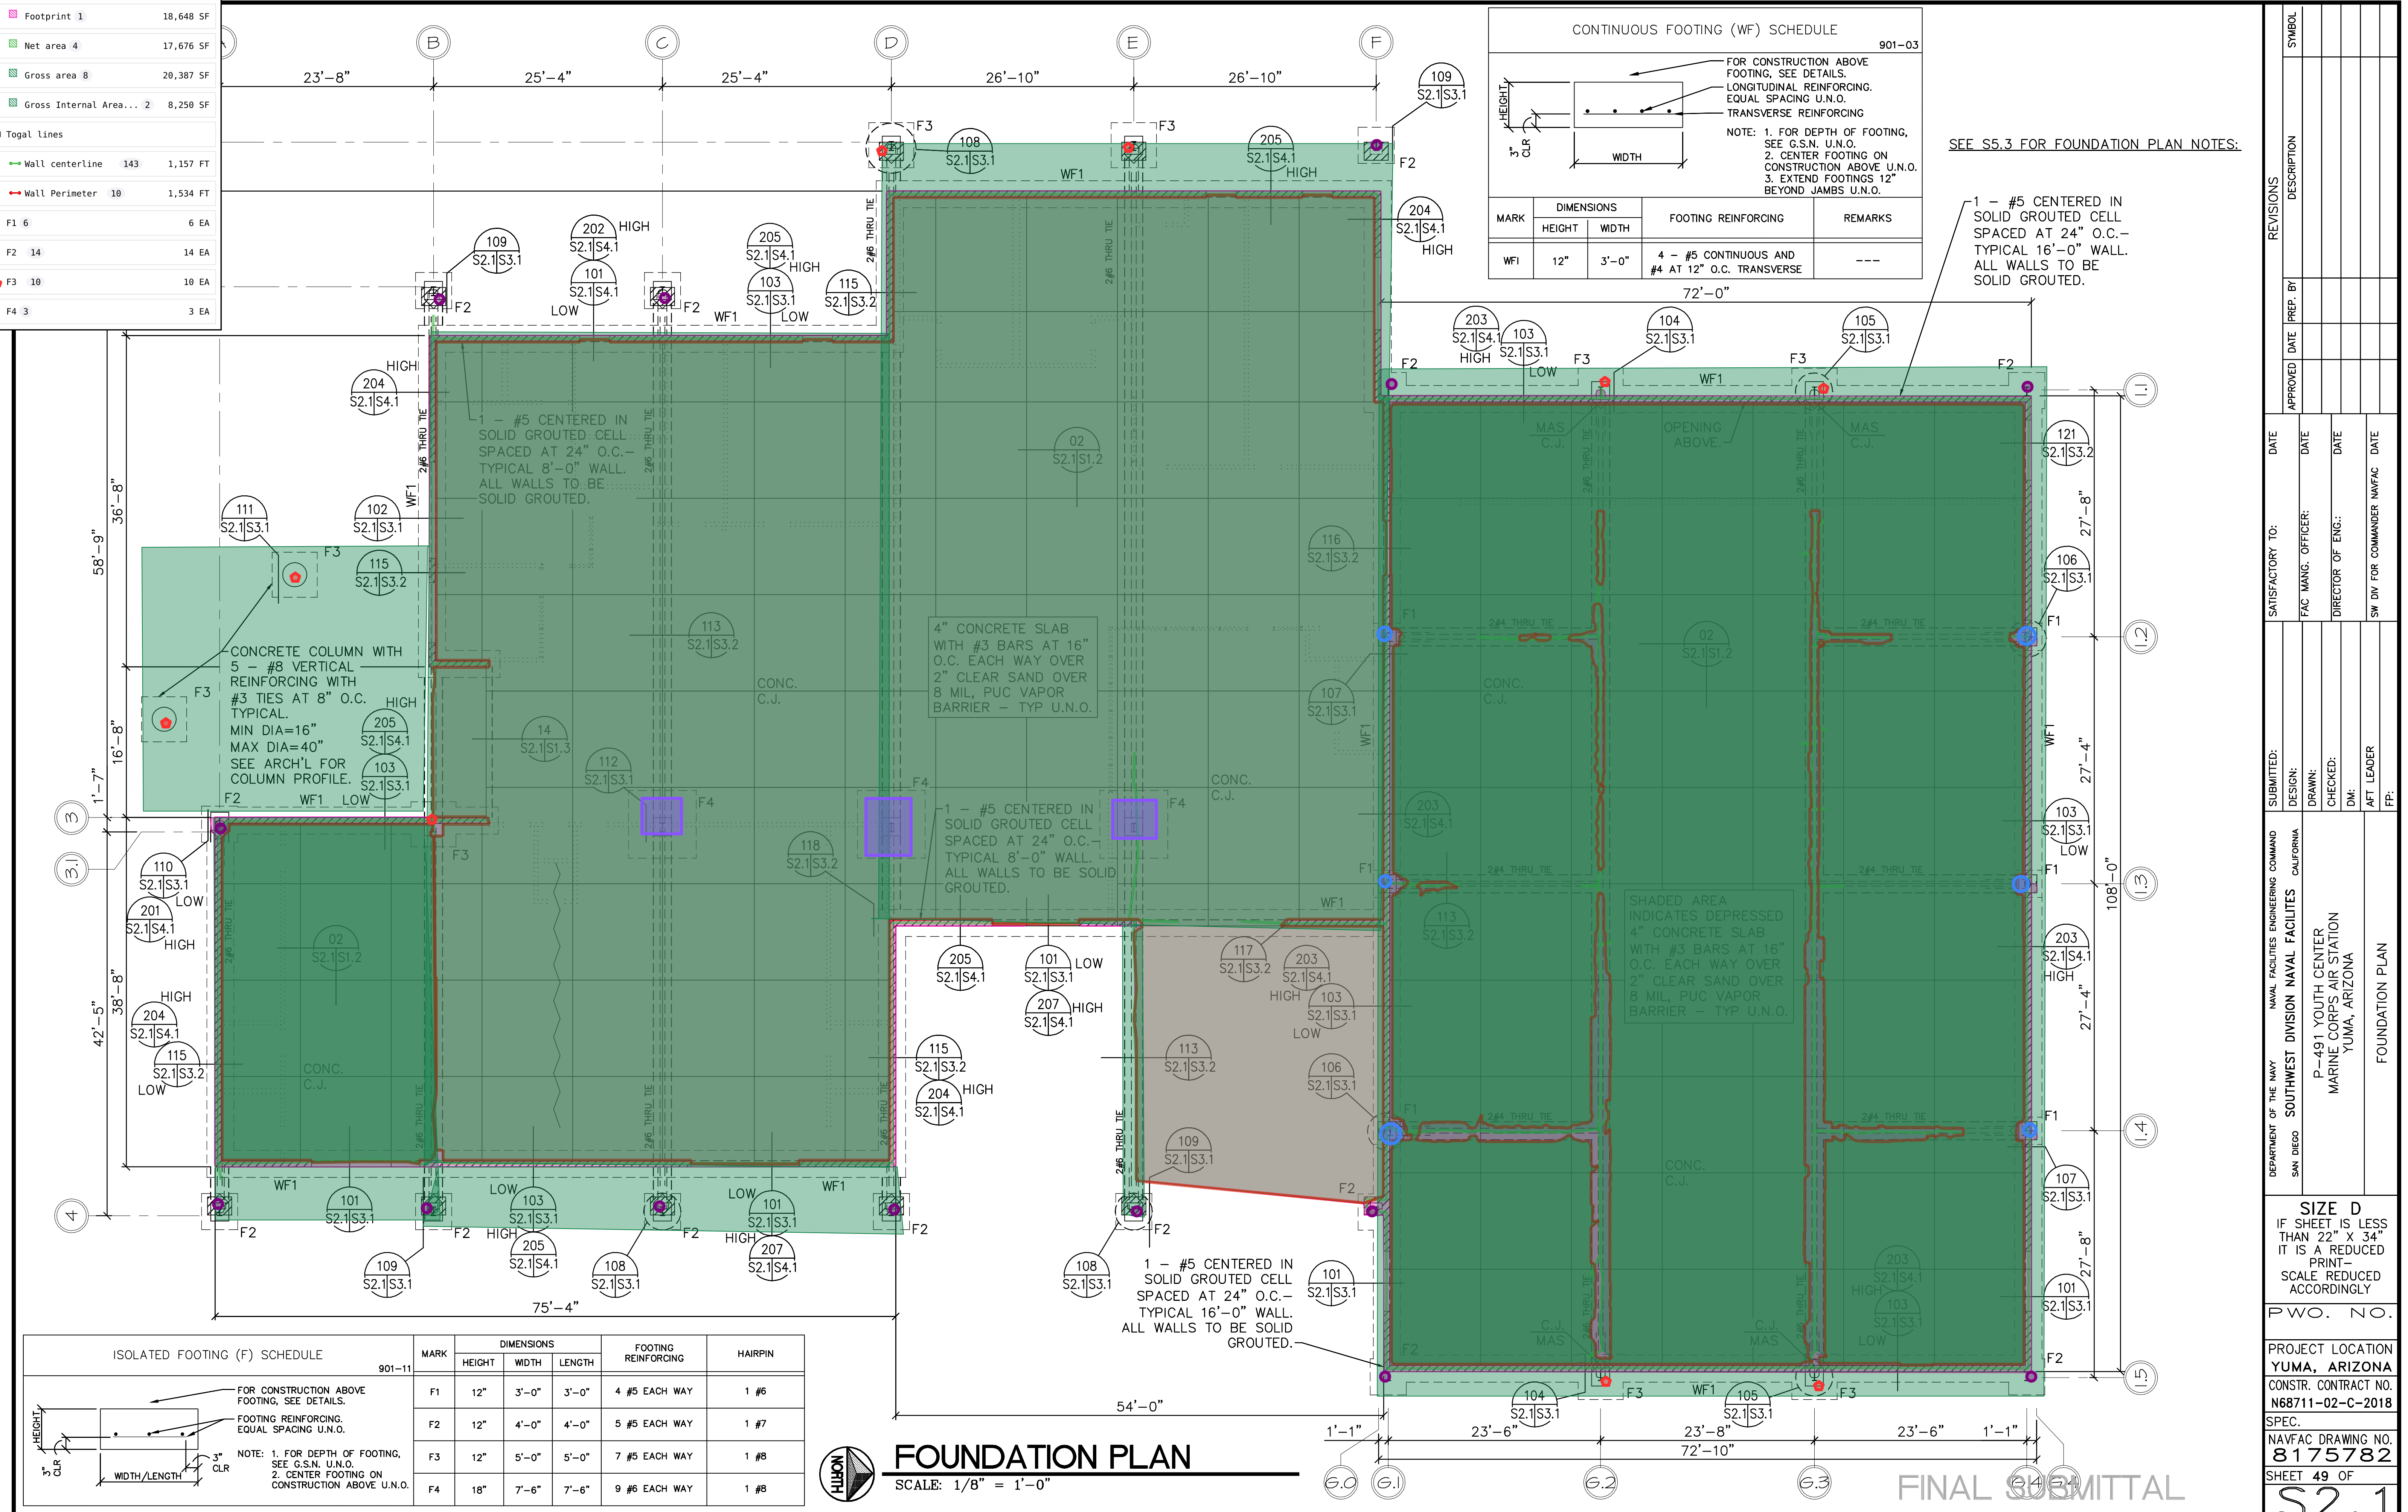

DEPARTMENT OF THE NAVY SAN DIEGO NAVAL FACILITIES ENGINEERING COMMAND CALIFORNIA SOUTHWEST DIVISION NAVAL FACILITIES						SUBMITTED:		SATISFACTORY TO:	DATE	REVISIONS			
						DESIGN:		FAC MANG. OFFICER:	DATE	APPROVED	PREP. BY	DESCRIPTION	SYMBOL
						DRAWN:							
						CHECKED:		DIRECTOR OF ENG.:	DATE				
						DM:							
						AFT LEADER		SW DIV FOR COMMANDER NAVFAC FP:	DATE				
						FP:							
SIZE D IF SHEET IS LESS THAN 22" x 34" IT IS A REDUCED PRINT - SCALE REDUCED ACCORDINGLY													
PWO. NO.													
PROJECT LOCATION YUMA, ARIZONA													
CONSTR. CONTRACT NO. N68711-02-C-2018													
SPEC.													
NAVFAC DRAWING NO. 8175782													
SHEET 49 OF 52													